

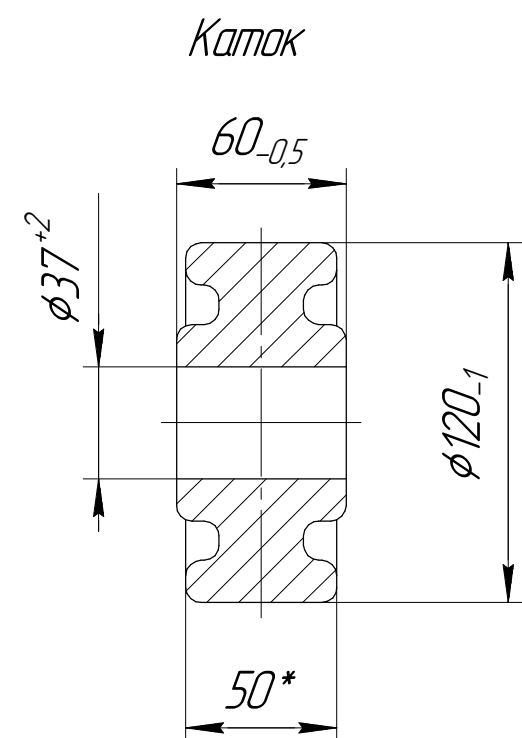
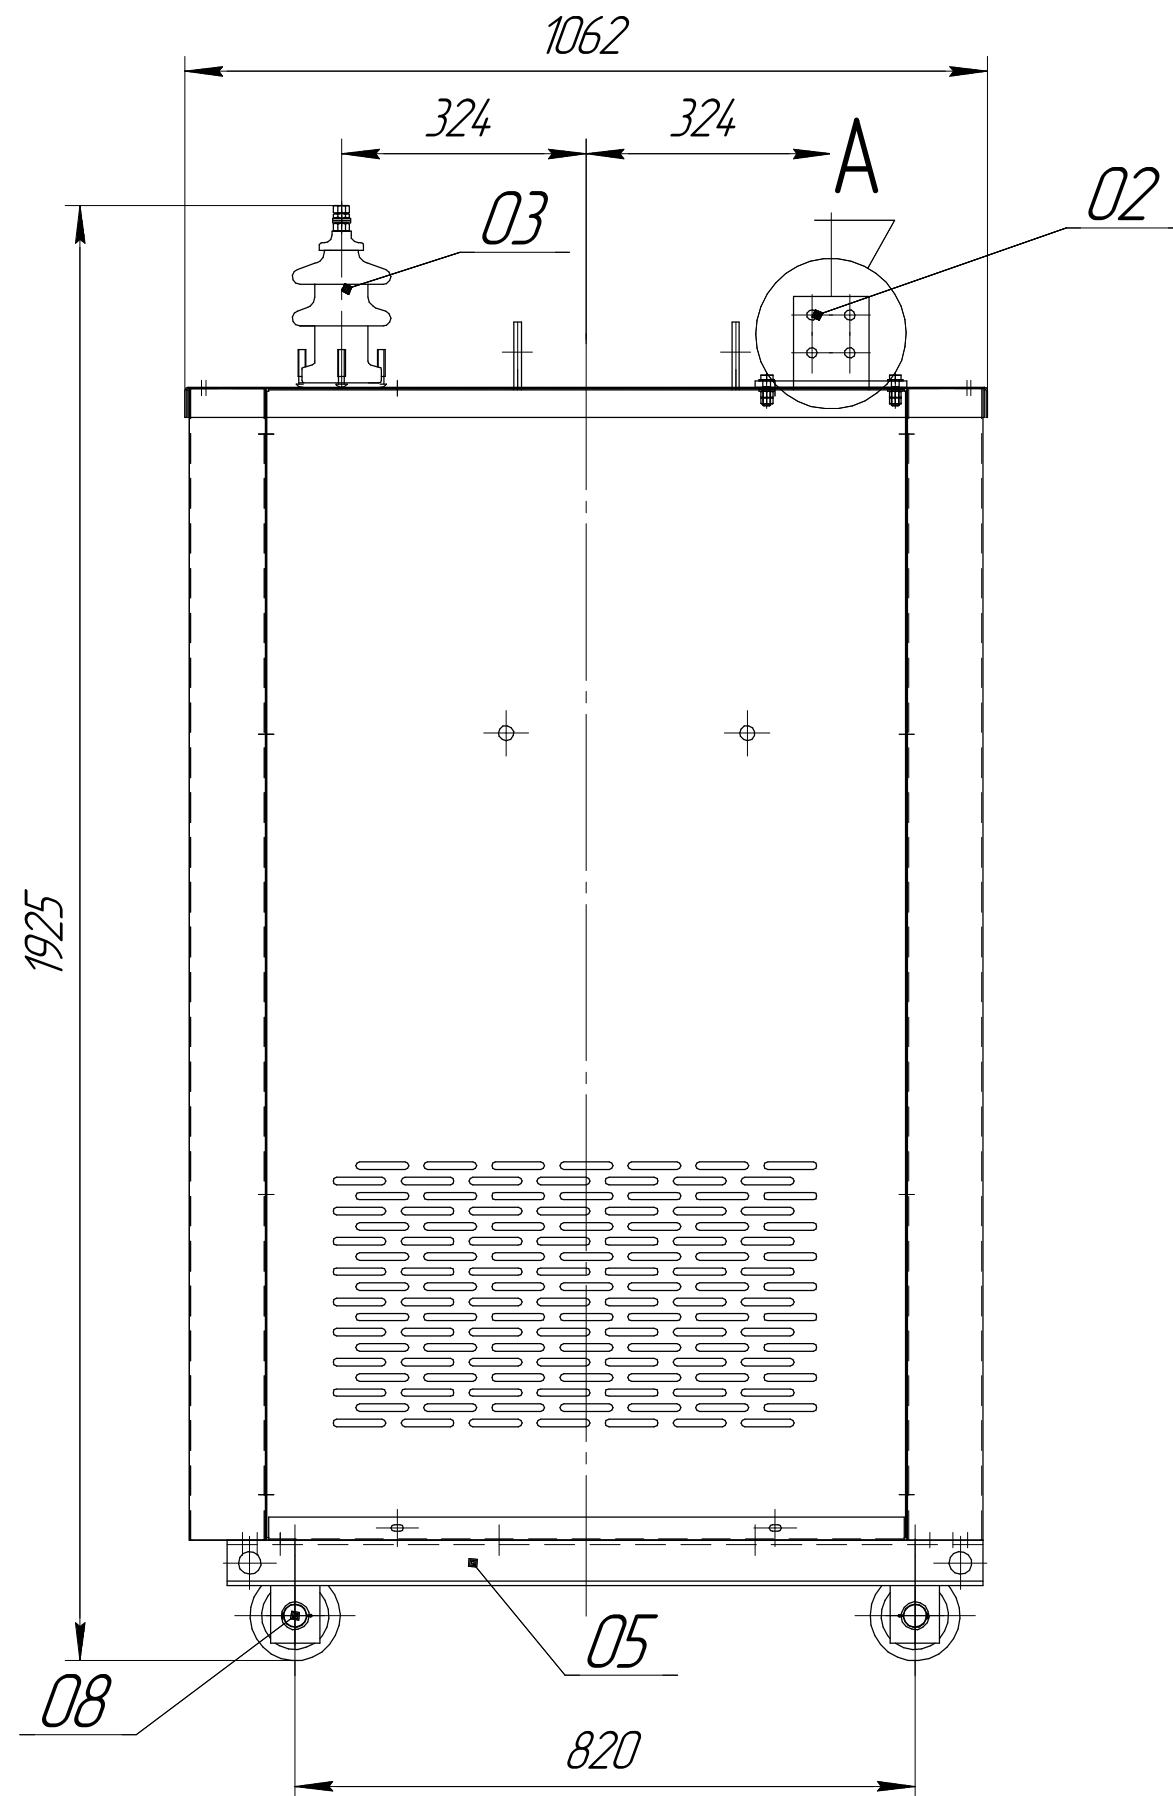


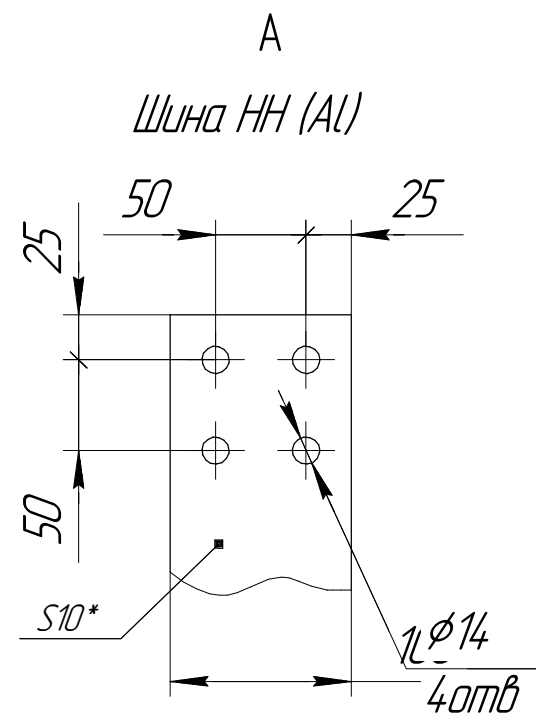

<i>Поз.</i>	<i>Наименование</i>
<i>01</i>	<i>Пластины подъемные</i>
<i>02</i>	<i>Вводы НН</i>
<i>03</i>	<i>Вводы ВН</i>
<i>04</i>	<i>Панель съёмная (доступ к ПБВ)</i>
<i>05</i>	<i>Балка подкареточная</i>
<i>06</i>	<i>Зажим заземления</i>
<i>07</i>	<i>Таблички технических данных</i>
<i>08</i>	<i>Катки (доп. опция)</i>

Чертеж является предварительным и может быть уточнен производителем в процессе проектирования.
За 15 дней до отгрузки необходимо подписать финальный чертеж с уточненными размерами.

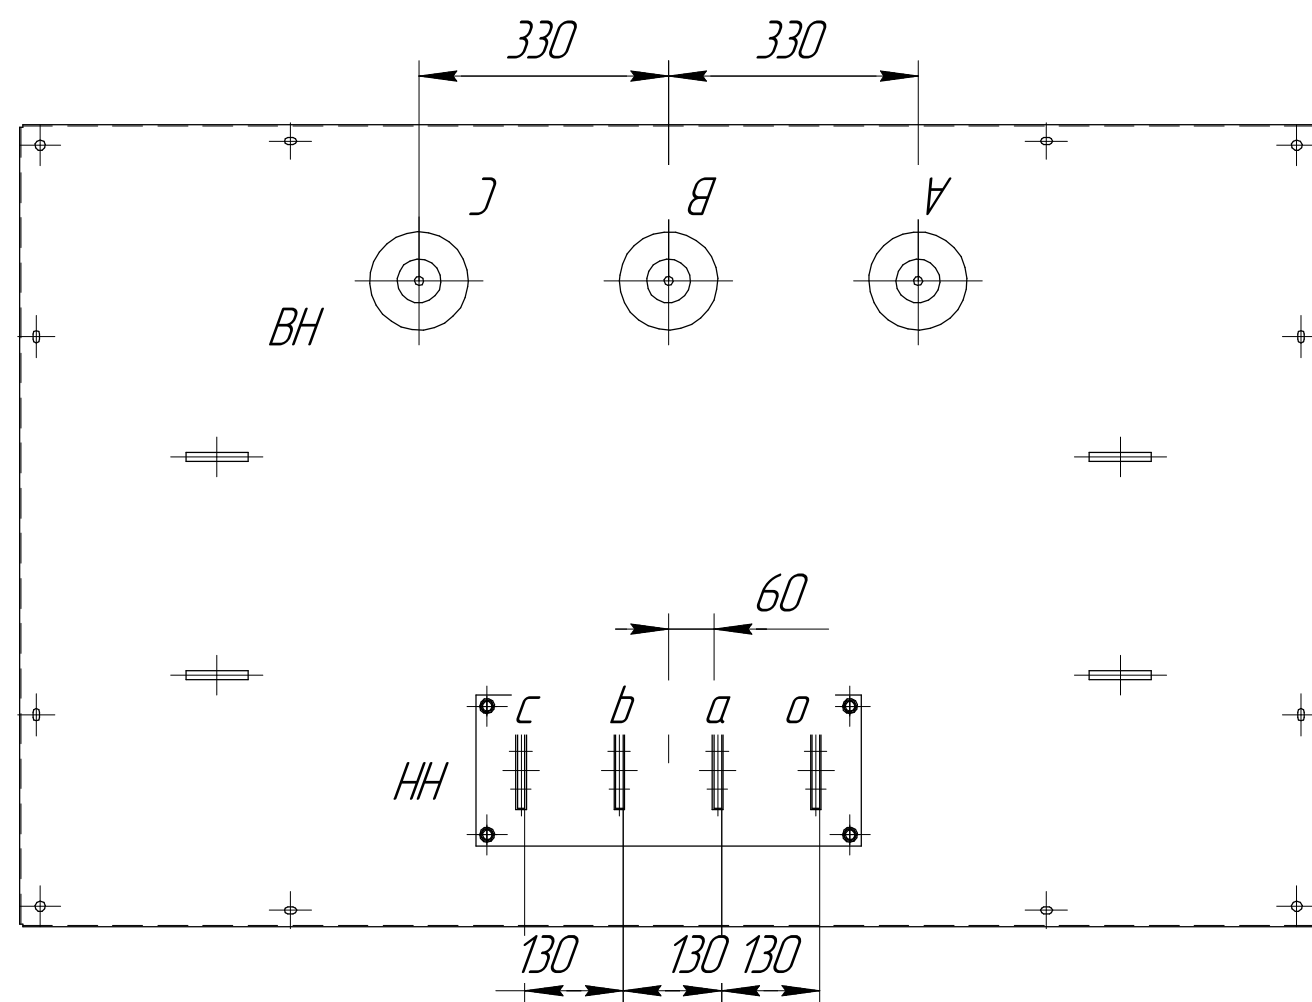

<i>Характеристики</i>	
$I_0, \%$	0,5
$U_k, \%$	6
$P_{x.x}, Bm$	2000
$P_{k.з}, Bm$	9400

						<i>Габаритный чертеж ГЧ</i>			
<i>Изм.</i>	<i>Лист</i>	<i>№ докум.</i>	<i>Подп.</i>	<i>Дата</i>	<i>ТС/З-1000/6, 10-0,4</i> <i>ВВ/ВВ-левое исполнение</i>	<i>Лит.</i>		<i>Масса</i>	<i>Масштаб</i>
<i>Разраб.</i>		<i>Толеген</i>					<i>А</i>	<i>2566</i>	<i>1:10</i>
<i>Пров.</i>						<i>Лист</i>		<i>Листов</i>	
<i>Т.контр.</i>								<i>1</i>	
<i>Н.контр.</i>									
<i>Утв.</i>					<i>Материал обмотки:</i> <i>алюминий</i>		<i>АО "КТЗ"</i>		
					<i>Копировал</i>	<i>Формат А2</i>			